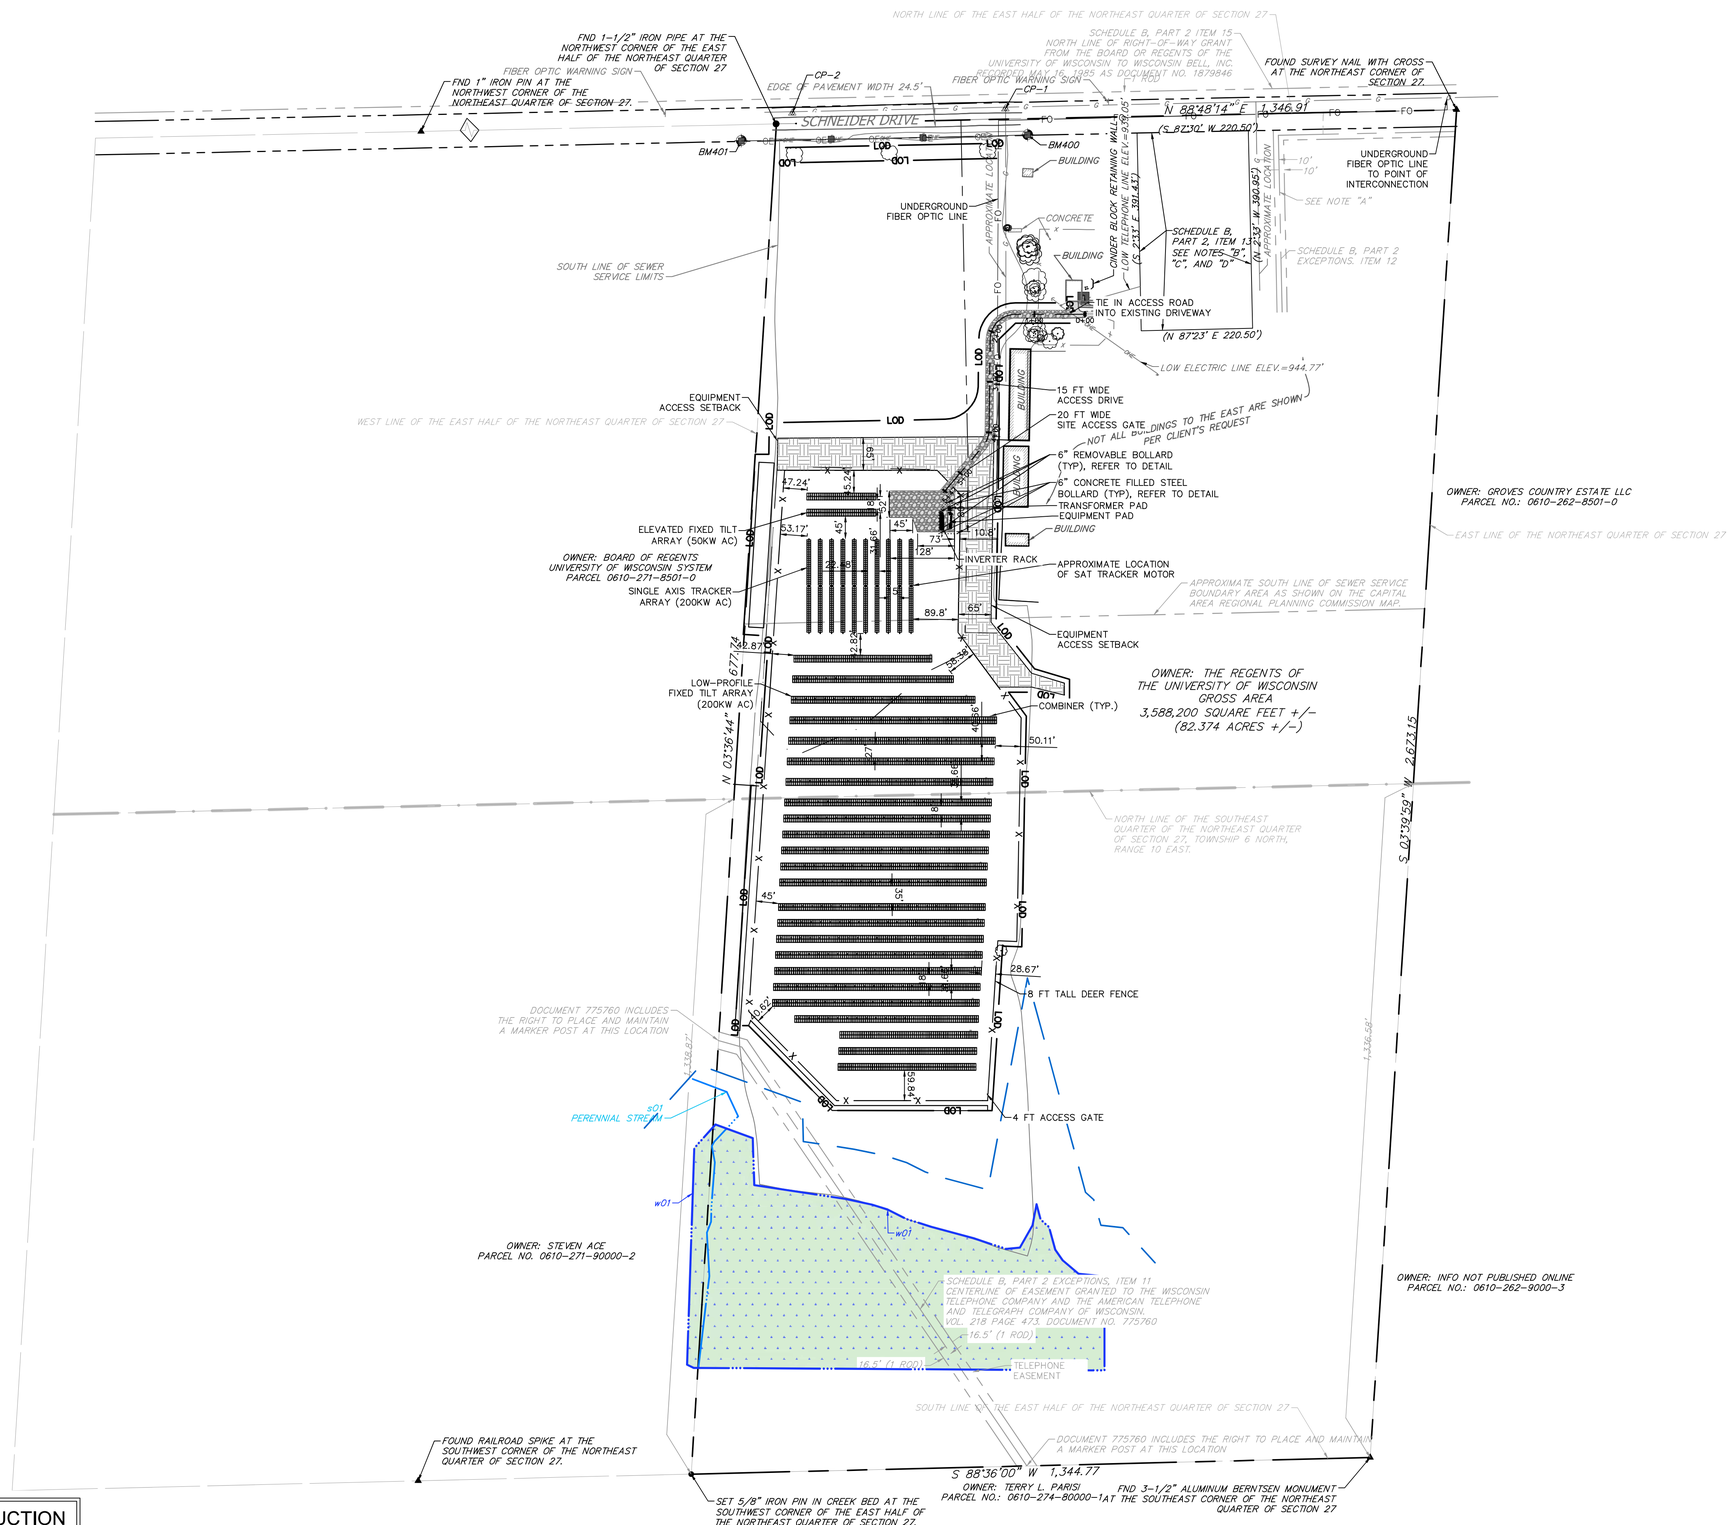

ISSUED FOR CONSTRUCTION

No.	Date	Revision
1	07/26/2024	REVISED STRUCTURAL RACKING DESIGN
2	08/15/2024	REVISED PER ALLIANT ENERGY / AHJ CMNTS
3	08/30/2024	REVISED LANDSCAPE

Seal

WISCONSIN CHAD ALBERTH E-49482 CANONSBURG PA PROFESSIONAL ENGINEER 08/30/24

Engineer

VERDANTERRA
2400 ANSYS DRIVE, STE. 401
CANONSBURG, PA 15317
724.916.4541
WWW.VERDANTERRA.COM

Applicant

SUNVEST SOLAR, LLC
N27 W24025 PAUL CT, SUITE 100
PEWAUKEE, WI 53072

Property Owners:

THE REGENTS OF THE UNIVERSITY OF WISCONSIN
3725 SCHNEIDER DRIVE
DUNN, WI 53589

Project Name:

KEGONSA SOLAR

Project Number: 06723011

Scale:	Drawn By:
AS NOTED	DJK
Date: MAY 2024	Checked By: CWC/SML

Drawing Description:

OVERALL SITE PLAN

Drawing Number:

C2.00

Sheet Number:

7 of 30